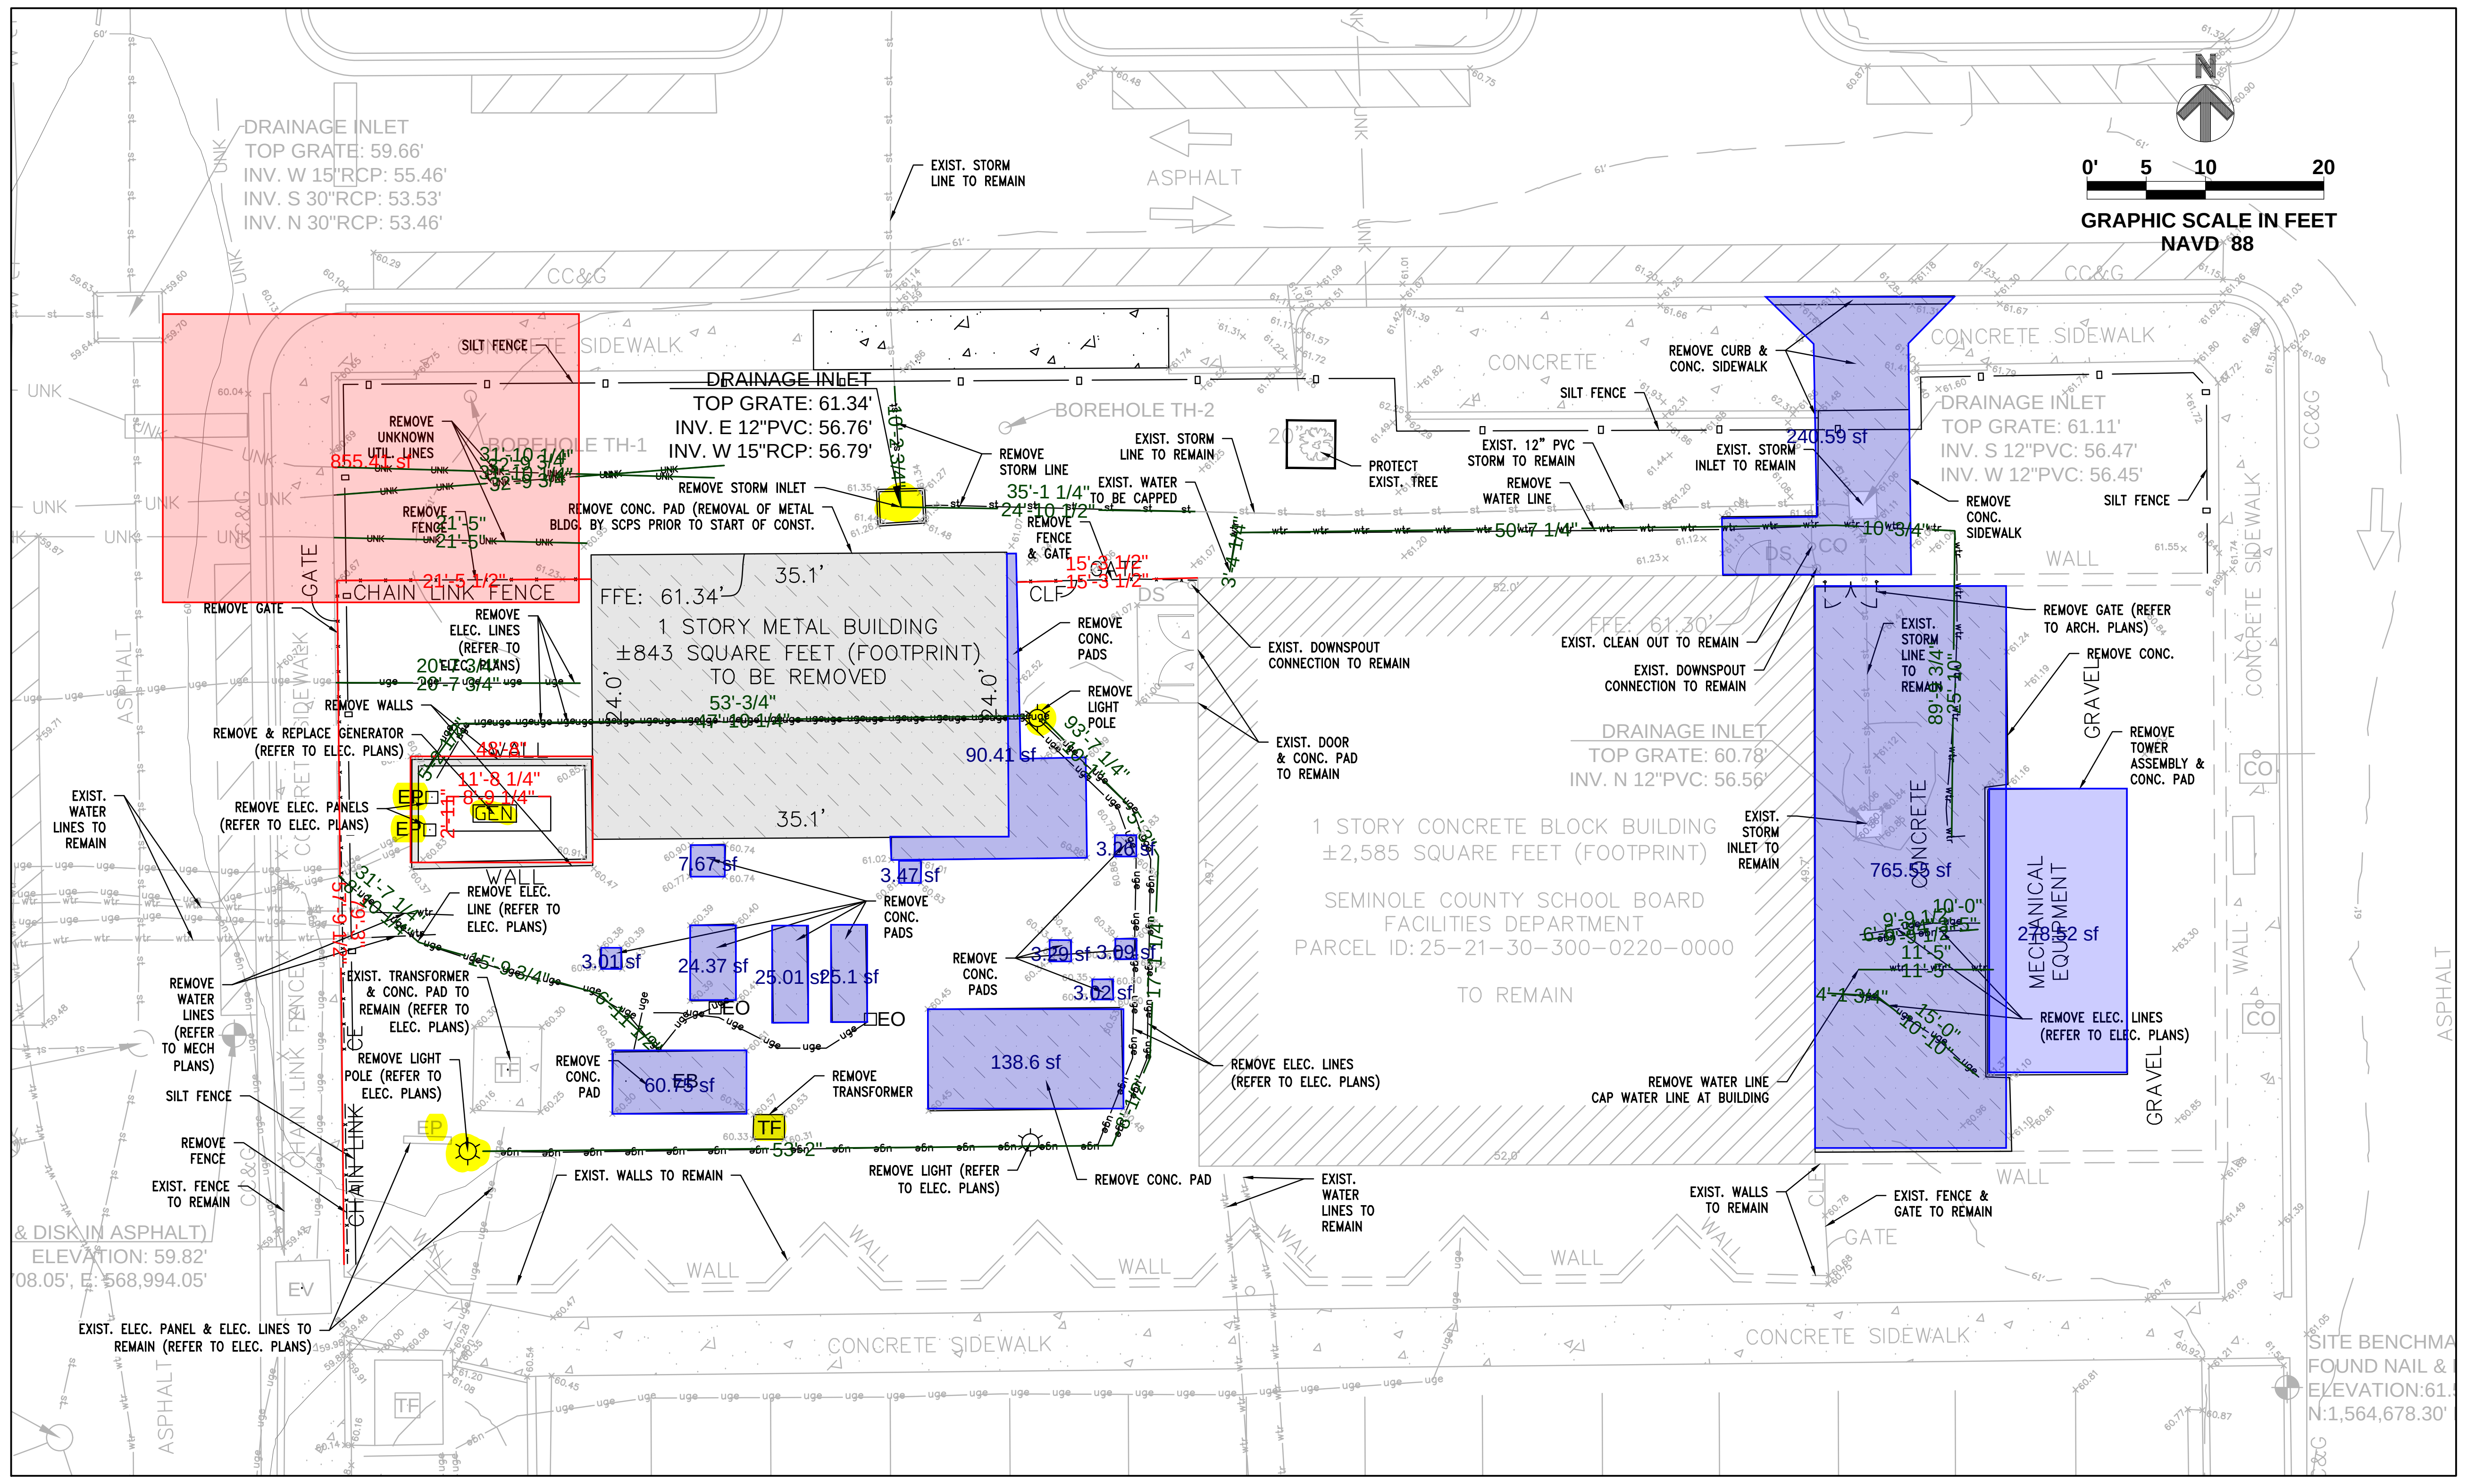

DEMOLITION PLAN

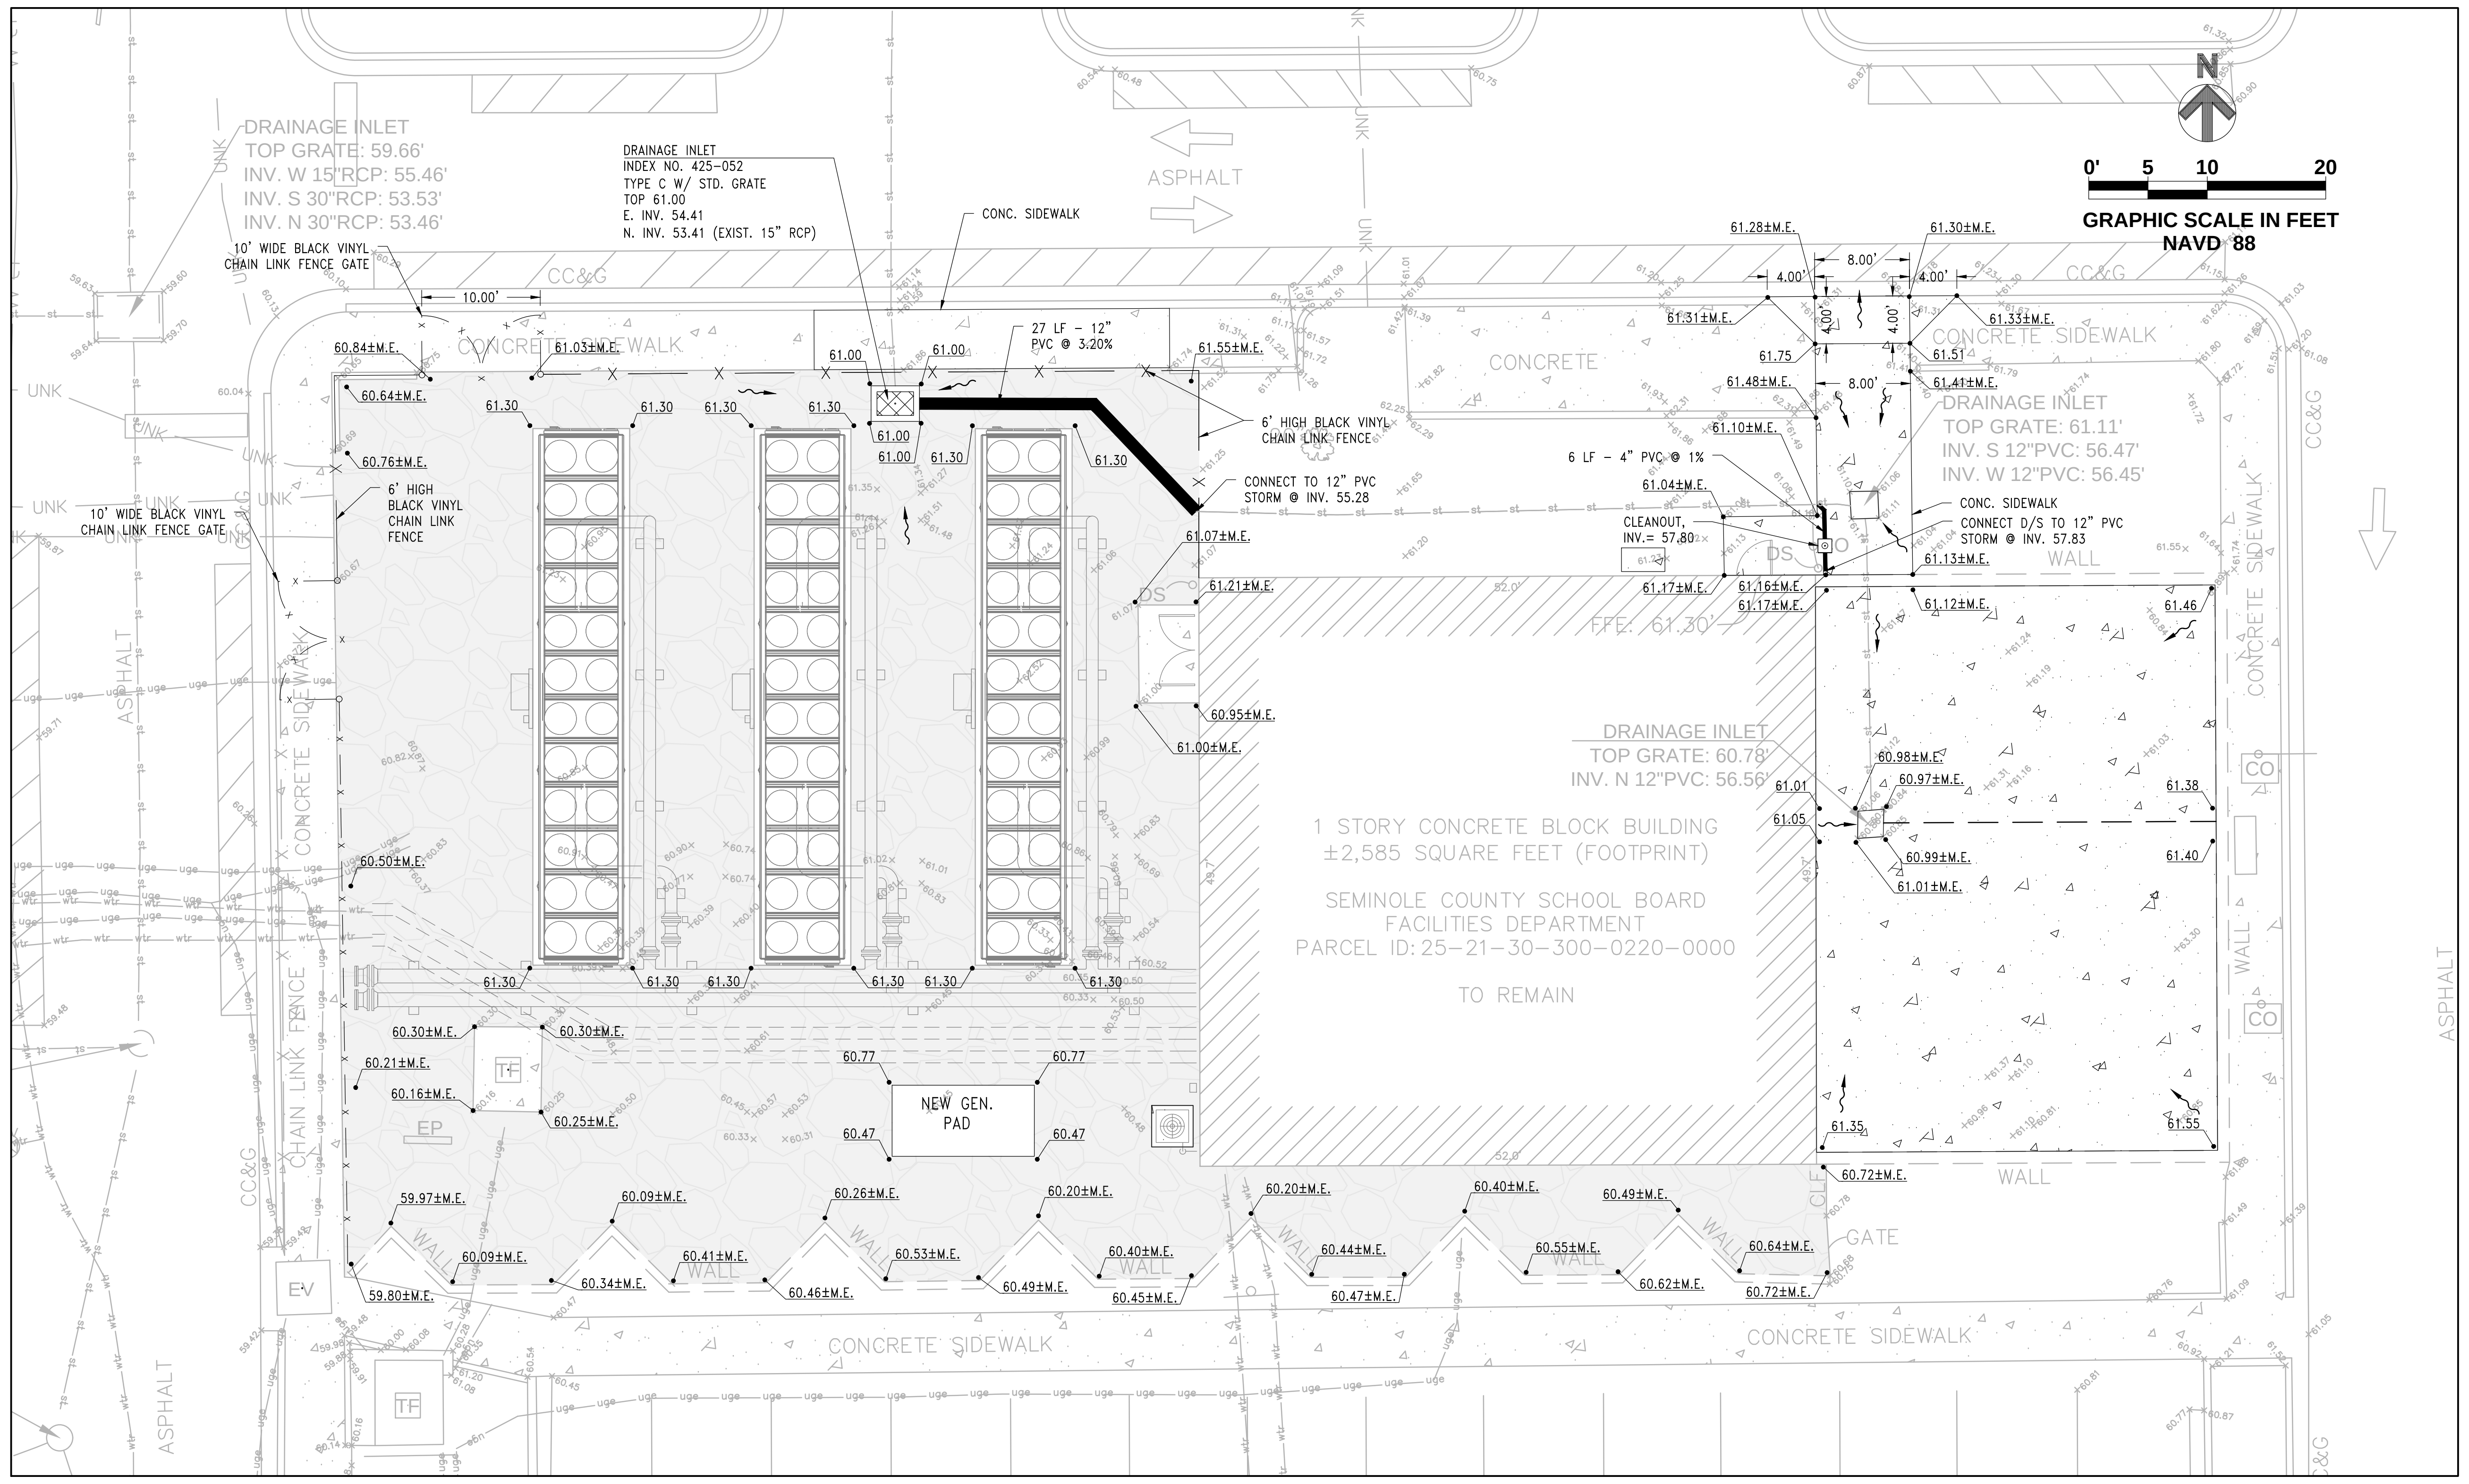
GRAPHIC SCALE IN FEET
0' 5 10 20
NAVD '88
DRAINAGE INLET
INDEX NO. 425-052
TYPE C W/ STD. GRATE
TOP 61.00
E. INV. 54.41
N. INV. 53.41 (EXIST. 15" RCP)
10' WIDE BLACK VINYL CHAIN LINK FENCE GATE
6' HIGH BLACK VINYL CHAIN LINK FENCE
27 LF – 12" PVC @ 3.20%
CONNECT TO 12" PVC STORM @ INV. 55.28
6 LF – 4" PVC @ 1%
CLEANOUT, INV.= 57.80
CONC. SIDEWALK
CONNECT D/S TO 12" PVC STORM @ INV. 57.83
NEW GEN. PAD
1 STORY CONCRETE BLOCK BUILDING
±2,585 SQUARE FEET (FOOTPRINT)
SEMINOLE COUNTY SCHOOL BOARD
FACILITIES DEPARTMENT
PARCEL ID: 25–21–30–300–0220–0000
TO REMAIN
CONCRETE SIDEWALK
ASPHALT
WALL

GRADING, DRAINAGE, GEOMETRY, & SITE PLAN

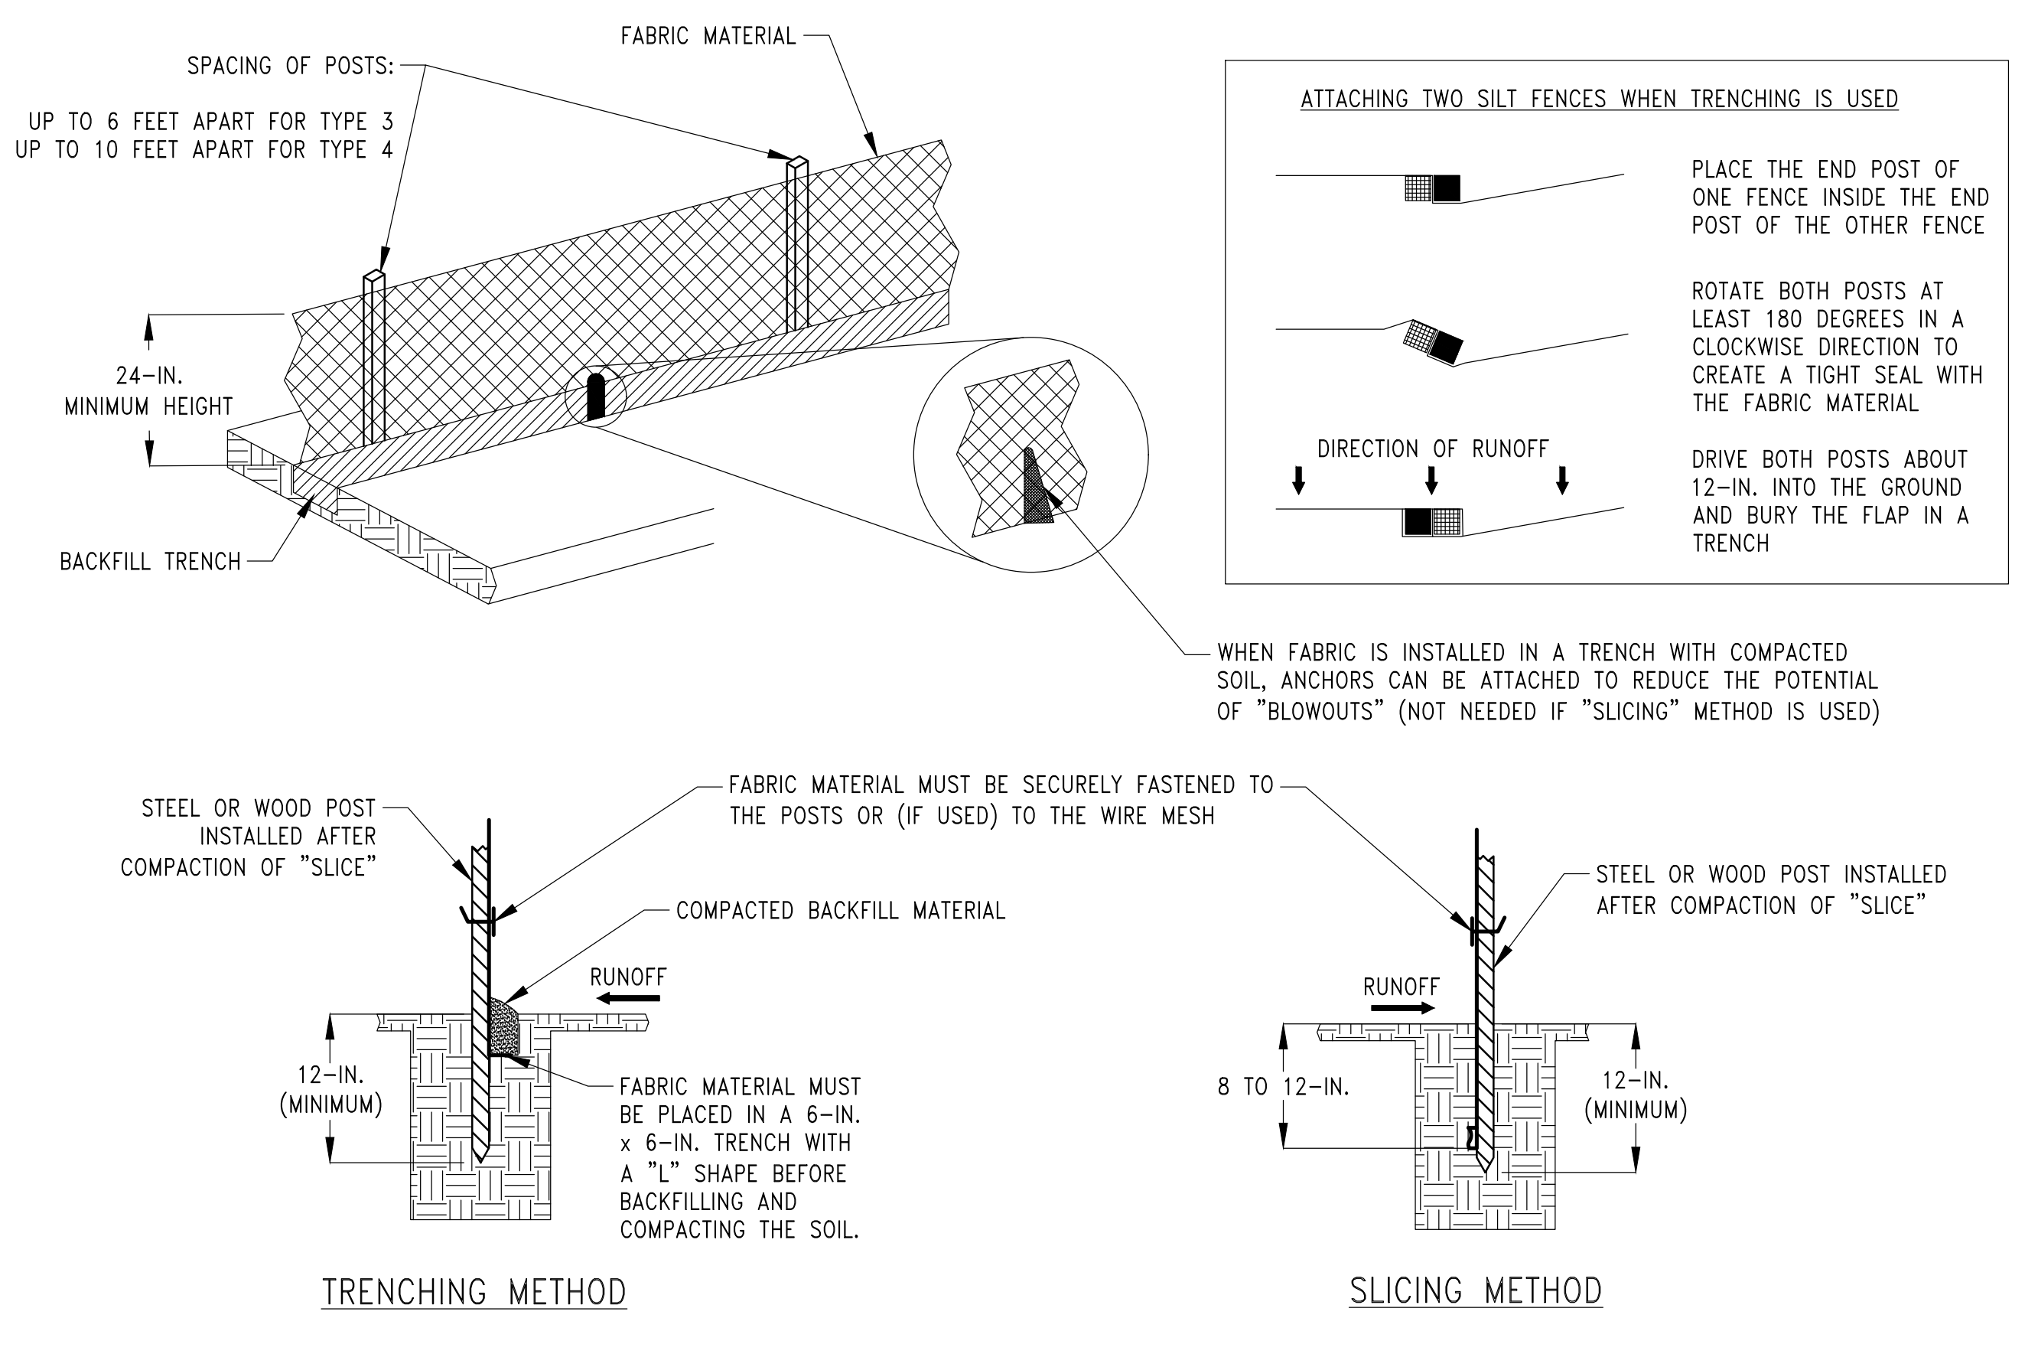
FABRIC MATERIAL
SPACING OF POSTS:
UP TO 6 FEET APART FOR TYPE 3
UP TO 10 FEET APART FOR TYPE 4
24–IN. MINIMUM HEIGHT
BACKFILL TRENCH
ATTACHING TWO SILT FENCES WHEN TRENCHING IS USED
PLACE THE END POST OF ONE FENCE INSIDE THE END POST OF THE OTHER FENCE
ROTATE BOTH POSTS AT LEAST 180 DEGREES IN A CLOCKWISE DIRECTION TO CREATE A TIGHT SEAL WITH THE FABRIC MATERIAL
DIRECTION OF RUNOFF
DRIVE BOTH POSTS ABOUT 12–IN. INTO THE GROUND AND BURY THE FLAP IN A TRENCH
WHEN FABRIC IS INSTALLED IN A TRENCH WITH COMPACTED SOIL, ANCHORS CAN BE ATTACHED TO REDUCE THE POTENTIAL OF "BLOWOUTS" (NOT NEEDED IF "SLICING" METHOD IS USED)
STEEL OR WOOD POST INSTALLED AFTER COMPACTION OF "SLICE"
FABRIC MATERIAL MUST BE SECURELY FASTENED TO THE POSTS OR (IF USED) TO THE WIRE MESH
COMPACTED BACKFILL MATERIAL
RUNOFF
12–IN. (MINIMUM)
FABRIC MATERIAL MUST BE PLACED IN A 6–IN. x 6–IN. TRENCH WITH A "L" SHAPE BEFORE BACKFILLING AND COMPACTING THE SOIL.
8 TO 12–IN.
TRENCHING METHOD
SLICING METHOD

SILT FENCE BARRIER INSTALLATION
N.T.S.

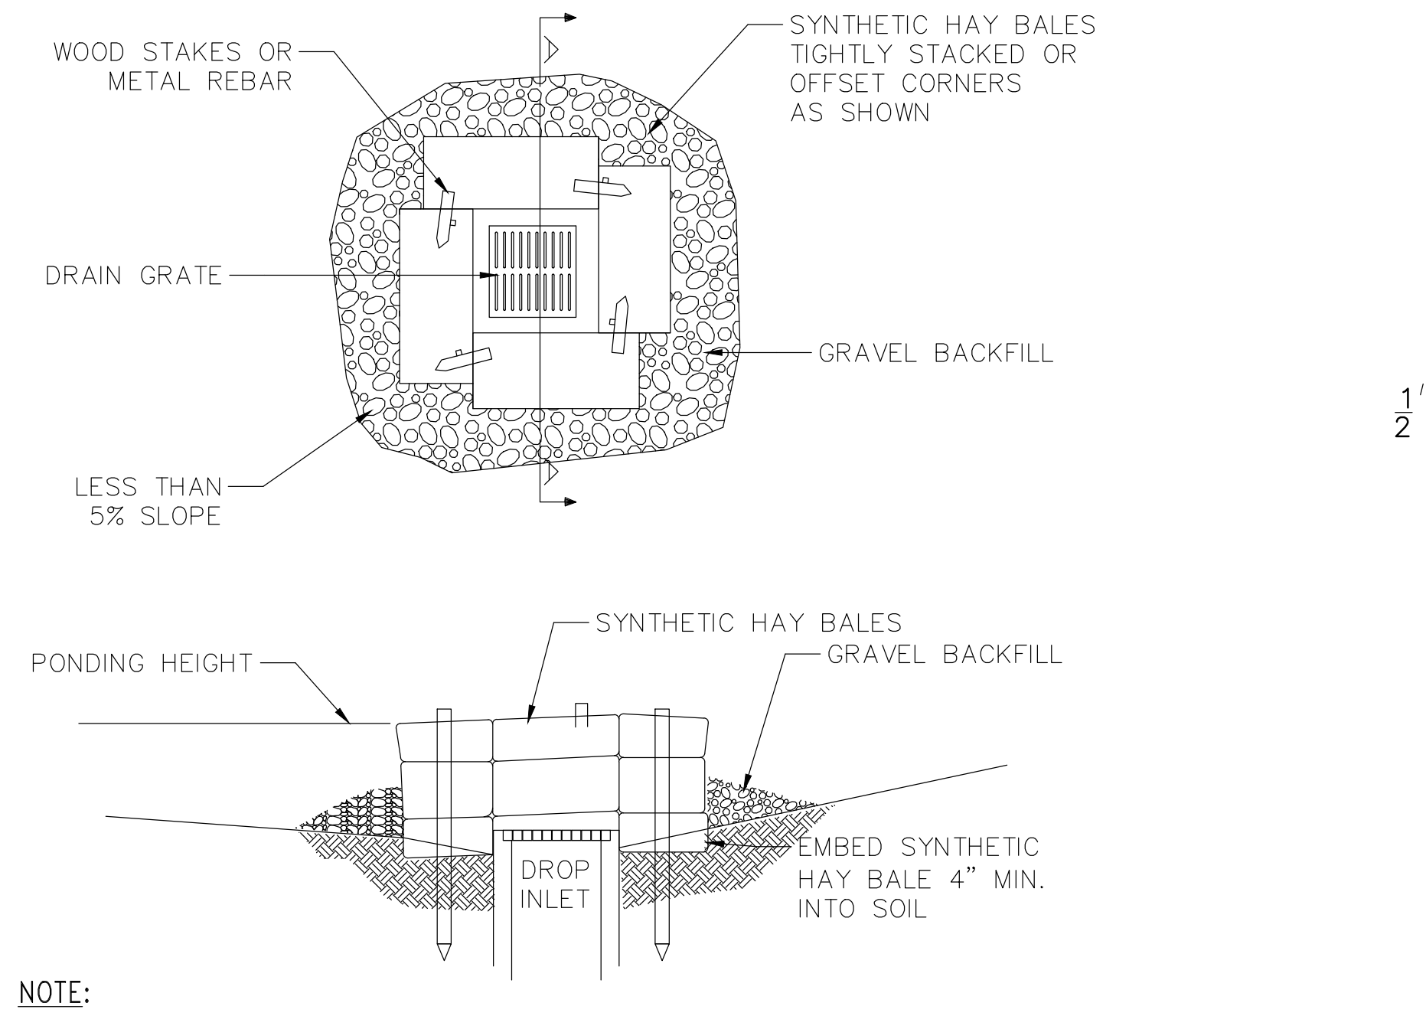
WOOD STAKES OR METAL REBAR
SYNTHETIC HAY BALES TIGHTLY STACKED OR OFFSET CORNERS AS SHOWN
DRAIN GRATE
GRAVEL BACKFILL
LESS THAN 5% SLOPE
PONDING HEIGHT
SYNTHETIC HAY BALES
GRAVEL BACKFILL
DROP INLET
EMBED SYNTHETIC HAY BALE 4" MIN. INTO SOIL

NOTE:

1. DROP INLET SEDIMENT BARRIERS ARE TO B EUSED FO RSMALL NEARLY LEVEL DRAINAGE AREAS. (LESS THAN 5%)
2. EMBED THE BALES 4" INTO THE SOIL AND OFFSET CORNERS OR PLACE BALES WITH ENDS TIGHTLY ABUTTING. GRAVEL BACKFILL WILL PREVENT EROSION OR FLOW AROUND THE BALES.
3. THE TOP OF THE STRUCTURE (PONDING HEIGHT) MUST BE WELL BELOW THE GROUND ELEVATION DOWN SLOPE TO PREVENT RUNOFF FROM BY-PASSING THE INLET. EXCAVATION OF A BASIN ADJACENT TO THE DROP INLET OR A TEMPORARY DIKE ON THE DOWN SLOPE OF THE STRUCTURE MAY BE NECESSARY.

DROP INLET SEDIMENT PROTECTION
N.T.S

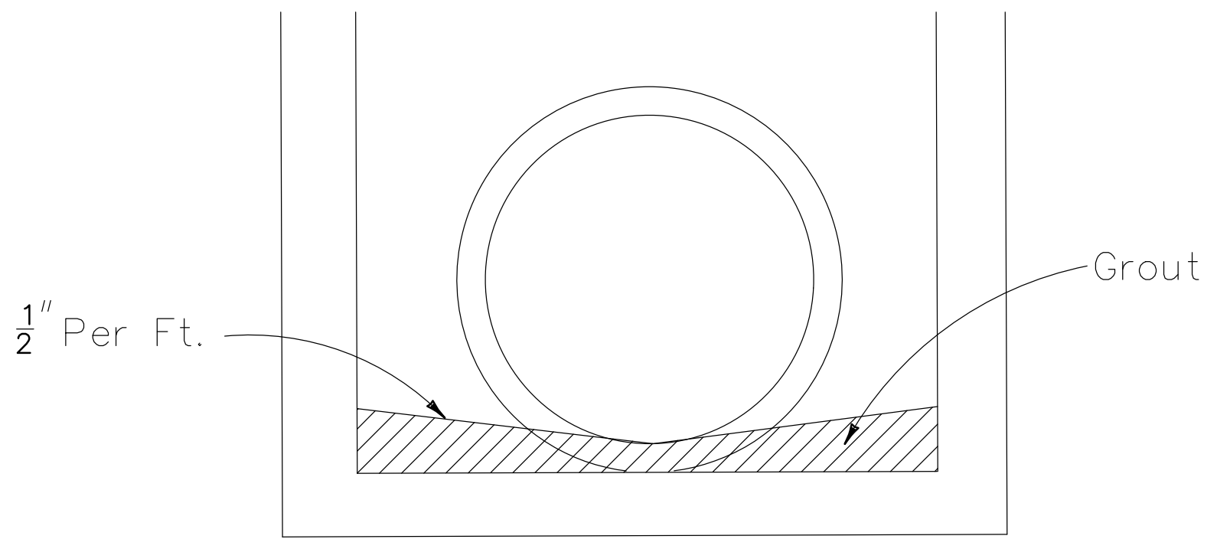

NOTE: GROUT TO CONSIST OF 3:1 SAND-CEMENT MIXTURE OR ANY CLASS CONCRETE FOR ALL STRUCTURES UNLESS EXCLUDED BY SPECIAL DETAIL.

DRAINAGE STRUCTURE INVERT
N.T.S.

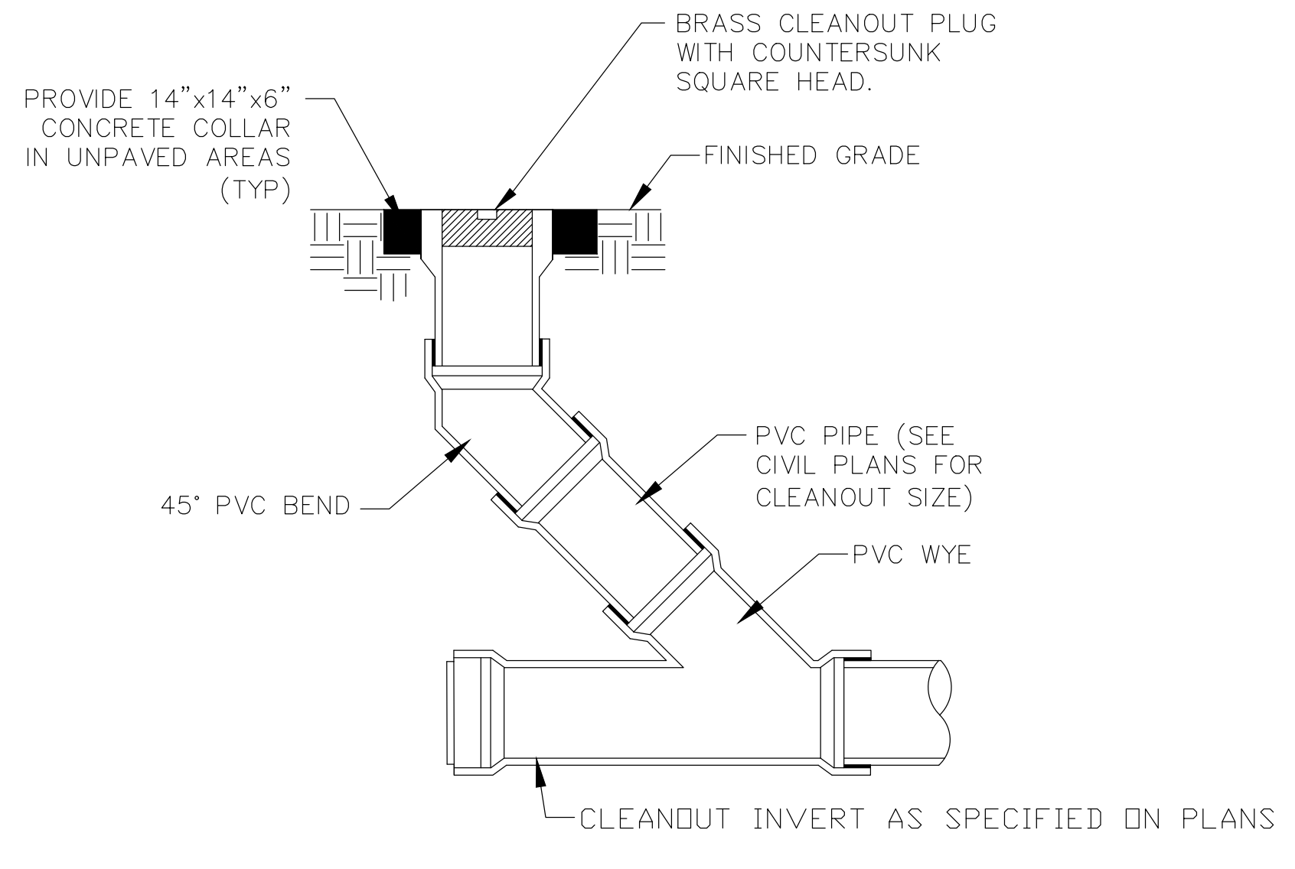
PROVIDE 14"x14"x6" CONCRETE COLLAR IN UNPAVED AREAS (TYP)
BRASS CLEANOUT PLUG WITH COUNTERSUNK SQUARE HEAD.
FINISHED GRADE
PVC PIPE (SEE CIVIL PLANS FOR CLEANOUT SIZE)
45° PVC BEND
PVC WYE
CLEANOUT INVERT AS SPECIFIED ON PLANS

STORM CLEANOUT DETAIL
N.T.S.

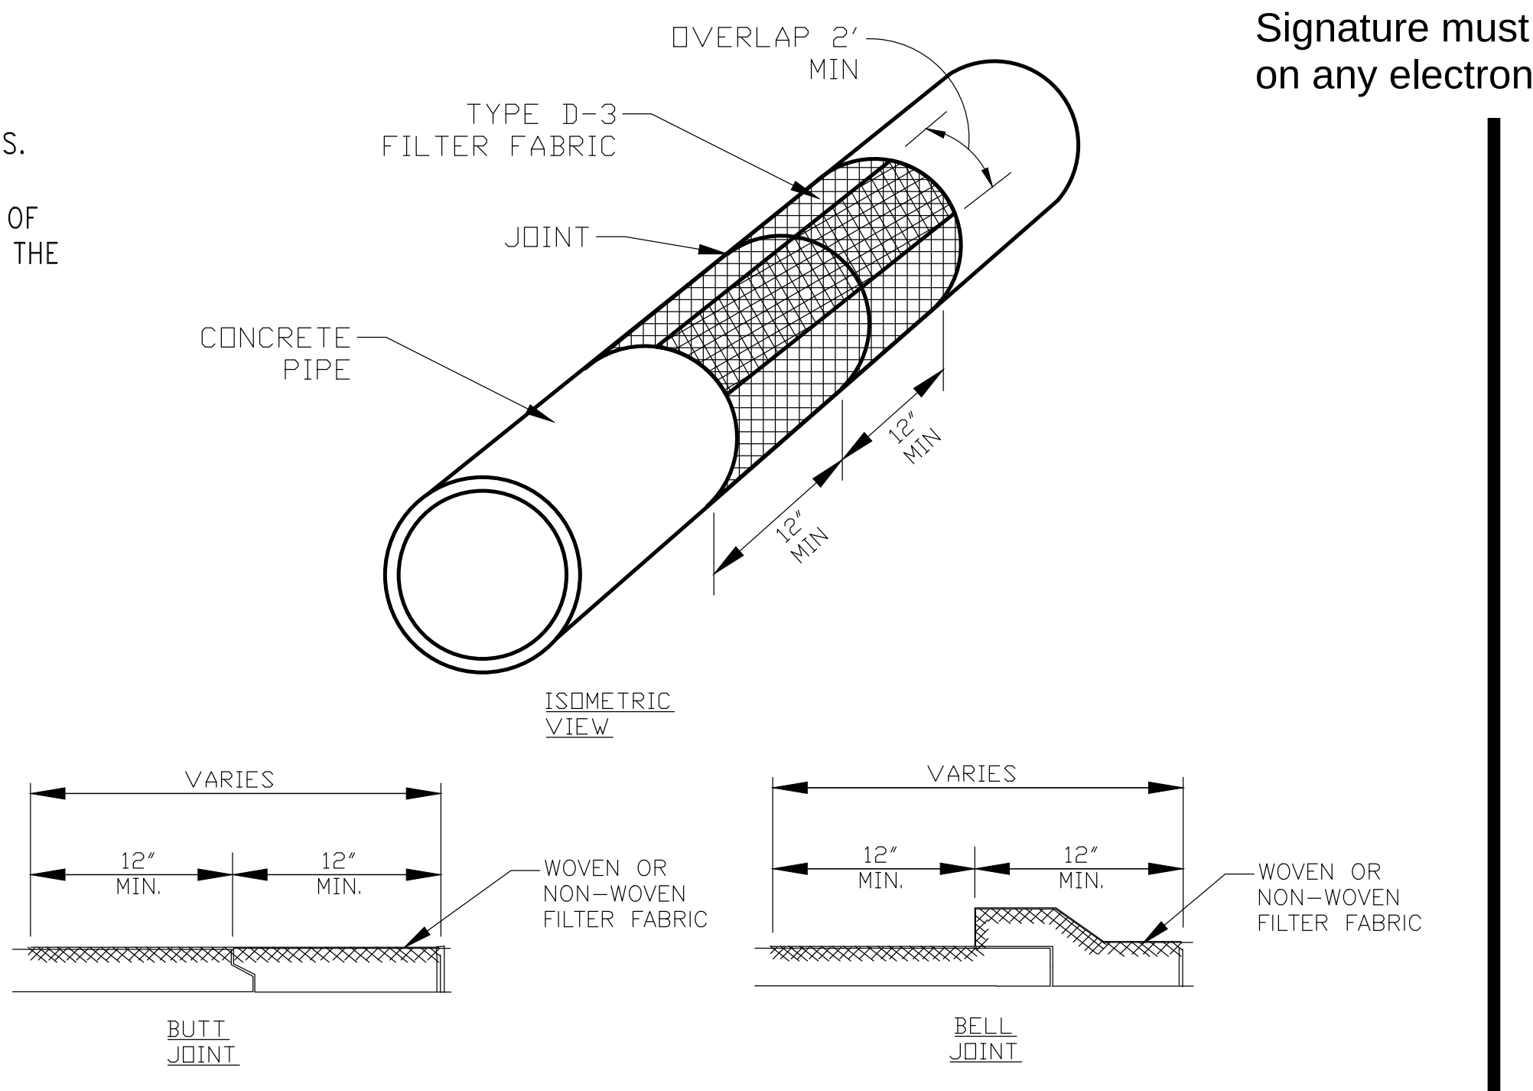

NOTE:

1. FILTER FABRIC MATERIAL MUST MEET THE FOLLOWING ASTM REQUIREMENTS: D-4595, D-4632, D-4533, D-4833, D-4491
2. FILTER FABRIC IS NOT REQUIRED WHEN AN O-RING GASKET IS USED.
3. FILTER FABRIC FOR THIS APPLICATION SHALL BE FDOT TYPE D-3.

FILTER FABRIC JACKET DETAIL
N.T.S.

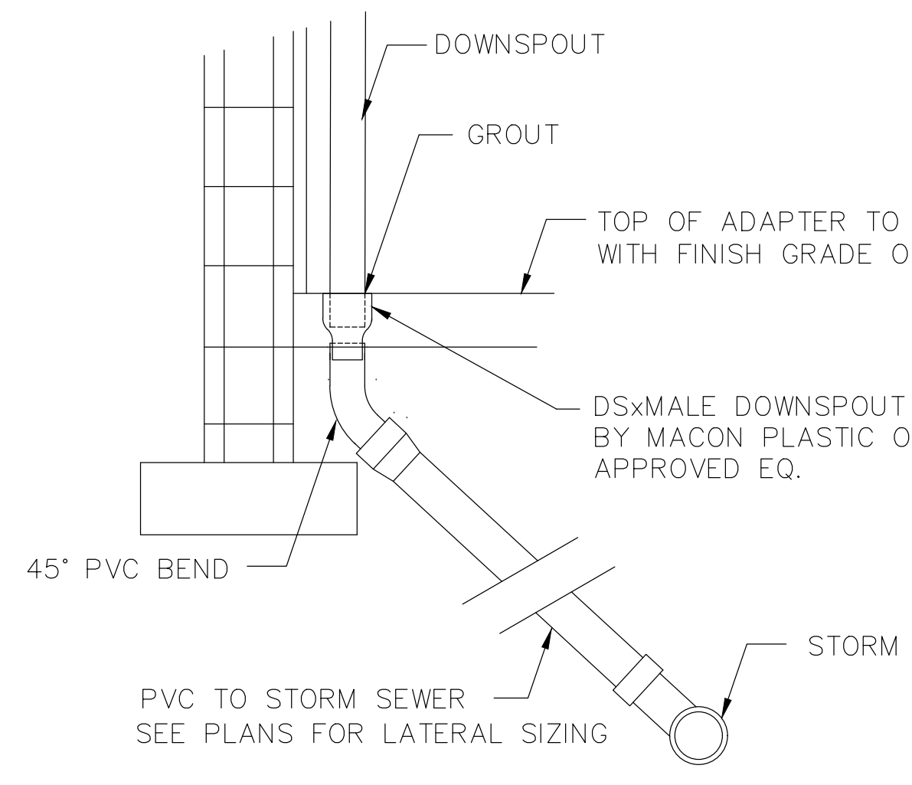
DOWNSPOUT
GROUT
TOP OF ADAPTER TO BE FLUSH WITH FINISH GRADE OF SIDEWALK
DSxMALE DOWNSPOUT ADAPTER BY MACON PLASTIC OR APPROVED EQ.
45° PVC BEND
STORM LINE
PVC TO STORM SEWER SEE PLANS FOR LATERAL SIZING

NOTES:

1. VERIFY THAT THERE ARE NO CONFLICTS WITH BUILDING/WALK FOUNDATION. PROVIDE FITTINGS AS REQUIRED TO MITIGATE CONFLICT.
2. ENSURE THAT CENTERLINE OF HUB MATCHES CENTERLINE OF DOWNSPOUT AT JUNCTION.
3. REFER TO ARCHITECTURAL PLANS FOR ADDITIONAL INFORMATION.

DOWNSPOUT CONNECTION DETAIL IN SIDEWALK
N.T.S.

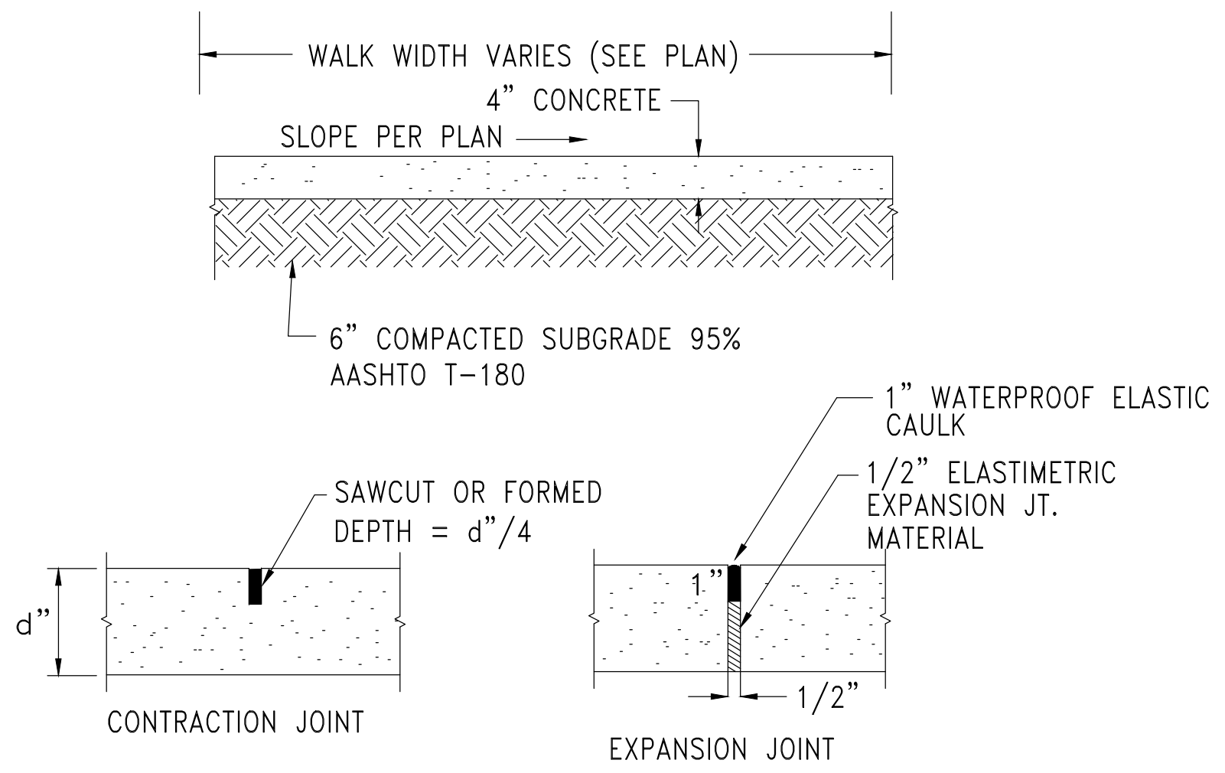
WALK WIDTH VARIES (SEE PLAN)
4" CONCRETE
SLOPE PER PLAN
6" COMPACTED SUBGRADE 95% AASHTO T-180
SAWCUT OR FORMED DEPTH = d"/4
d"
CONTRACTION JOINT
1" WATERPROOF ELASTIC CAULK
1/2" ELASTIMETRIC EXPANSION JT. MATERIAL
1"
1/2"
EXPANSION JOINT

NOTE:

1. ALL CONCRETE SIDEWALKS SHALL HAVE A FULL 1/2" EXPANSION JOINT AT A MAXIMUM DISTANCE OF 40 LINEAR FEET AND A SAW CUT OR FORMED DUMMY CONTRACTION JOINT AT EVENLY SPACED INTERVALS NOT TO EXCEED 8 LINEAR FEET.
2. CONTR. SHALL PROVIDE A MINIMUM OF 5 FT ON EITHER SIDE OF WALKS ADJACENT TO GRASS AREAS THAT HAVE A MAX. SLOPE OF 3% DOWNWARD.
2. CONCRETE PAVEMENT TO BE 3,000-PSI COMPRESSIVE STRENGTH, MIN.

CONCRETE SIDEWALK DETAILS
N.T.S.

LEGEND

▨	LIMITS OF CLEARING (REMOVAL OF SITE DEBRIS, CONCRETE, PAVEMENT, WALKS, FENCE, BUILDING, TREES, ETC.)
—▫—▫—	SILT FENCE
☐	TREE PROTECTION
12.00±M.E.	MATCH EXISTING GRADE
12.00	PROPOSED SPOT GRADE
×11.00	EXISTING SPOT GRADE
∿→	PROPOSED DRAINAGE FLOW
◎	MANHOLE
▭ ▣	INLET
▬	PVC
– – – –	GRADE BREAK
—x—x—	CHAIN LINK FENCE
▨	6" THICK CONCRETE
▨	6" THICK #57 STONE, USE MIRAFI 140N FILTER FABRIC

MATERN
Mechanical • Electrical • Plumbing • Fire Protection
Technology • Commissioning • Energy Engineers

130 Candace Drive
Maitland, FL 32751
ENG. BUS. No. EB-0005096 PHONE (407) 740-5020
CERT. OF AUTH. No. 5096 FAX (407) 740-0365

THIS DRAWING IS THE PROPERTY OF MATERN PROFESSIONAL ENGINEERING, INC. UNLESS OTHERWISE PROVIDED BY THE CONTRACT, THE CONTENTS OF THIS DRAWING SHALL NOT BE TRANSMITTED TO ANY OTHER PARTY EXCEPT AS AGREED TO BY THE ENGINEER.

SCPS LAKE HOWELL HS CEP REPLACEMENT

Seminole County Public Schools

385 DOUGLAS AVENUE
ALTAMONTE SPRINGS
TELEPHONE 407
FACSIMILE 407
www.klimaw
Klima Weeks
CIVIL ENGINEERING

This item has been digitally signed and sealed by JAY A. KLIMA on the date adjacent to the seal.

Signature must be verified on any electronic copies.

No. 49945

JAY A. KLIMA, P.E.
FL P.E. #49945

Revisions

No.	Date	Description

MPE PROJ#: 2025–073
Designed By: JDO
Drawn By: JONEALL
Checked By:
Issue Date: 02/18/2026
Drawing Scale: AS NOTED

Drawing Title:
SITE PLAN

Drawing No.
C100

P:\LAND PROJECTS 2025\25MATE018 - LH HS CEP\DWG\C100 - SITE PLAN - LHCEP.DWG
19/02/2026